


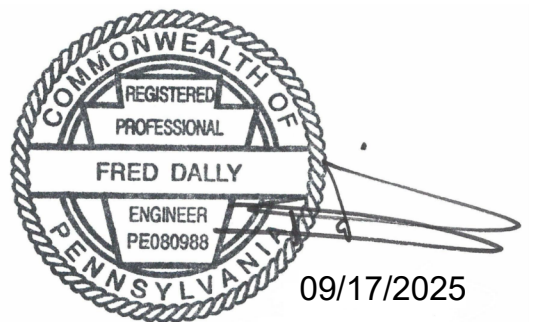

Consultants

Structural Engineer

Dally + Associates

9800 Richmond Avenue Suite 460

Houston, Texas 77042

MEP Engineer and Technology

Telios

730 Town and Country Blvd, Suite

750 Houston, TX 77042

Civil Engineers

Bohler

1515 Market Street, Suite 920

Philadelphia, PA 19102

[illegible]

Project

Emerus
Springfield
Neighborhood
Hospital

Christiana Care Community

Hospital

Springfield, PA 19064

Drawing Name

SECOND FLOOR
FRAMING PLAN - AREA
A


Copyright (C) 2024 by PhiloWike Partnership. All rights reserved.

This document and the information herein is the property of PhiloWike Partnership. No part hereof shall be copied, duplicated, distributed, disclosed or used to any extent whatsoever except as expressly authorized by PhiloWike Partnership. Any Person, firm, or corporation receiving this document, however obtained, shall by virtue hereof, be deemed to have agreed to the foregoing restrictions and that this document will be held in trust and confidence subject only to the private use expressly authorized by PhiloWike Partnership.

Print Date / Time: 9/17/2025 12:02:13 PM

Philo/Wilke Commission Number

S202A

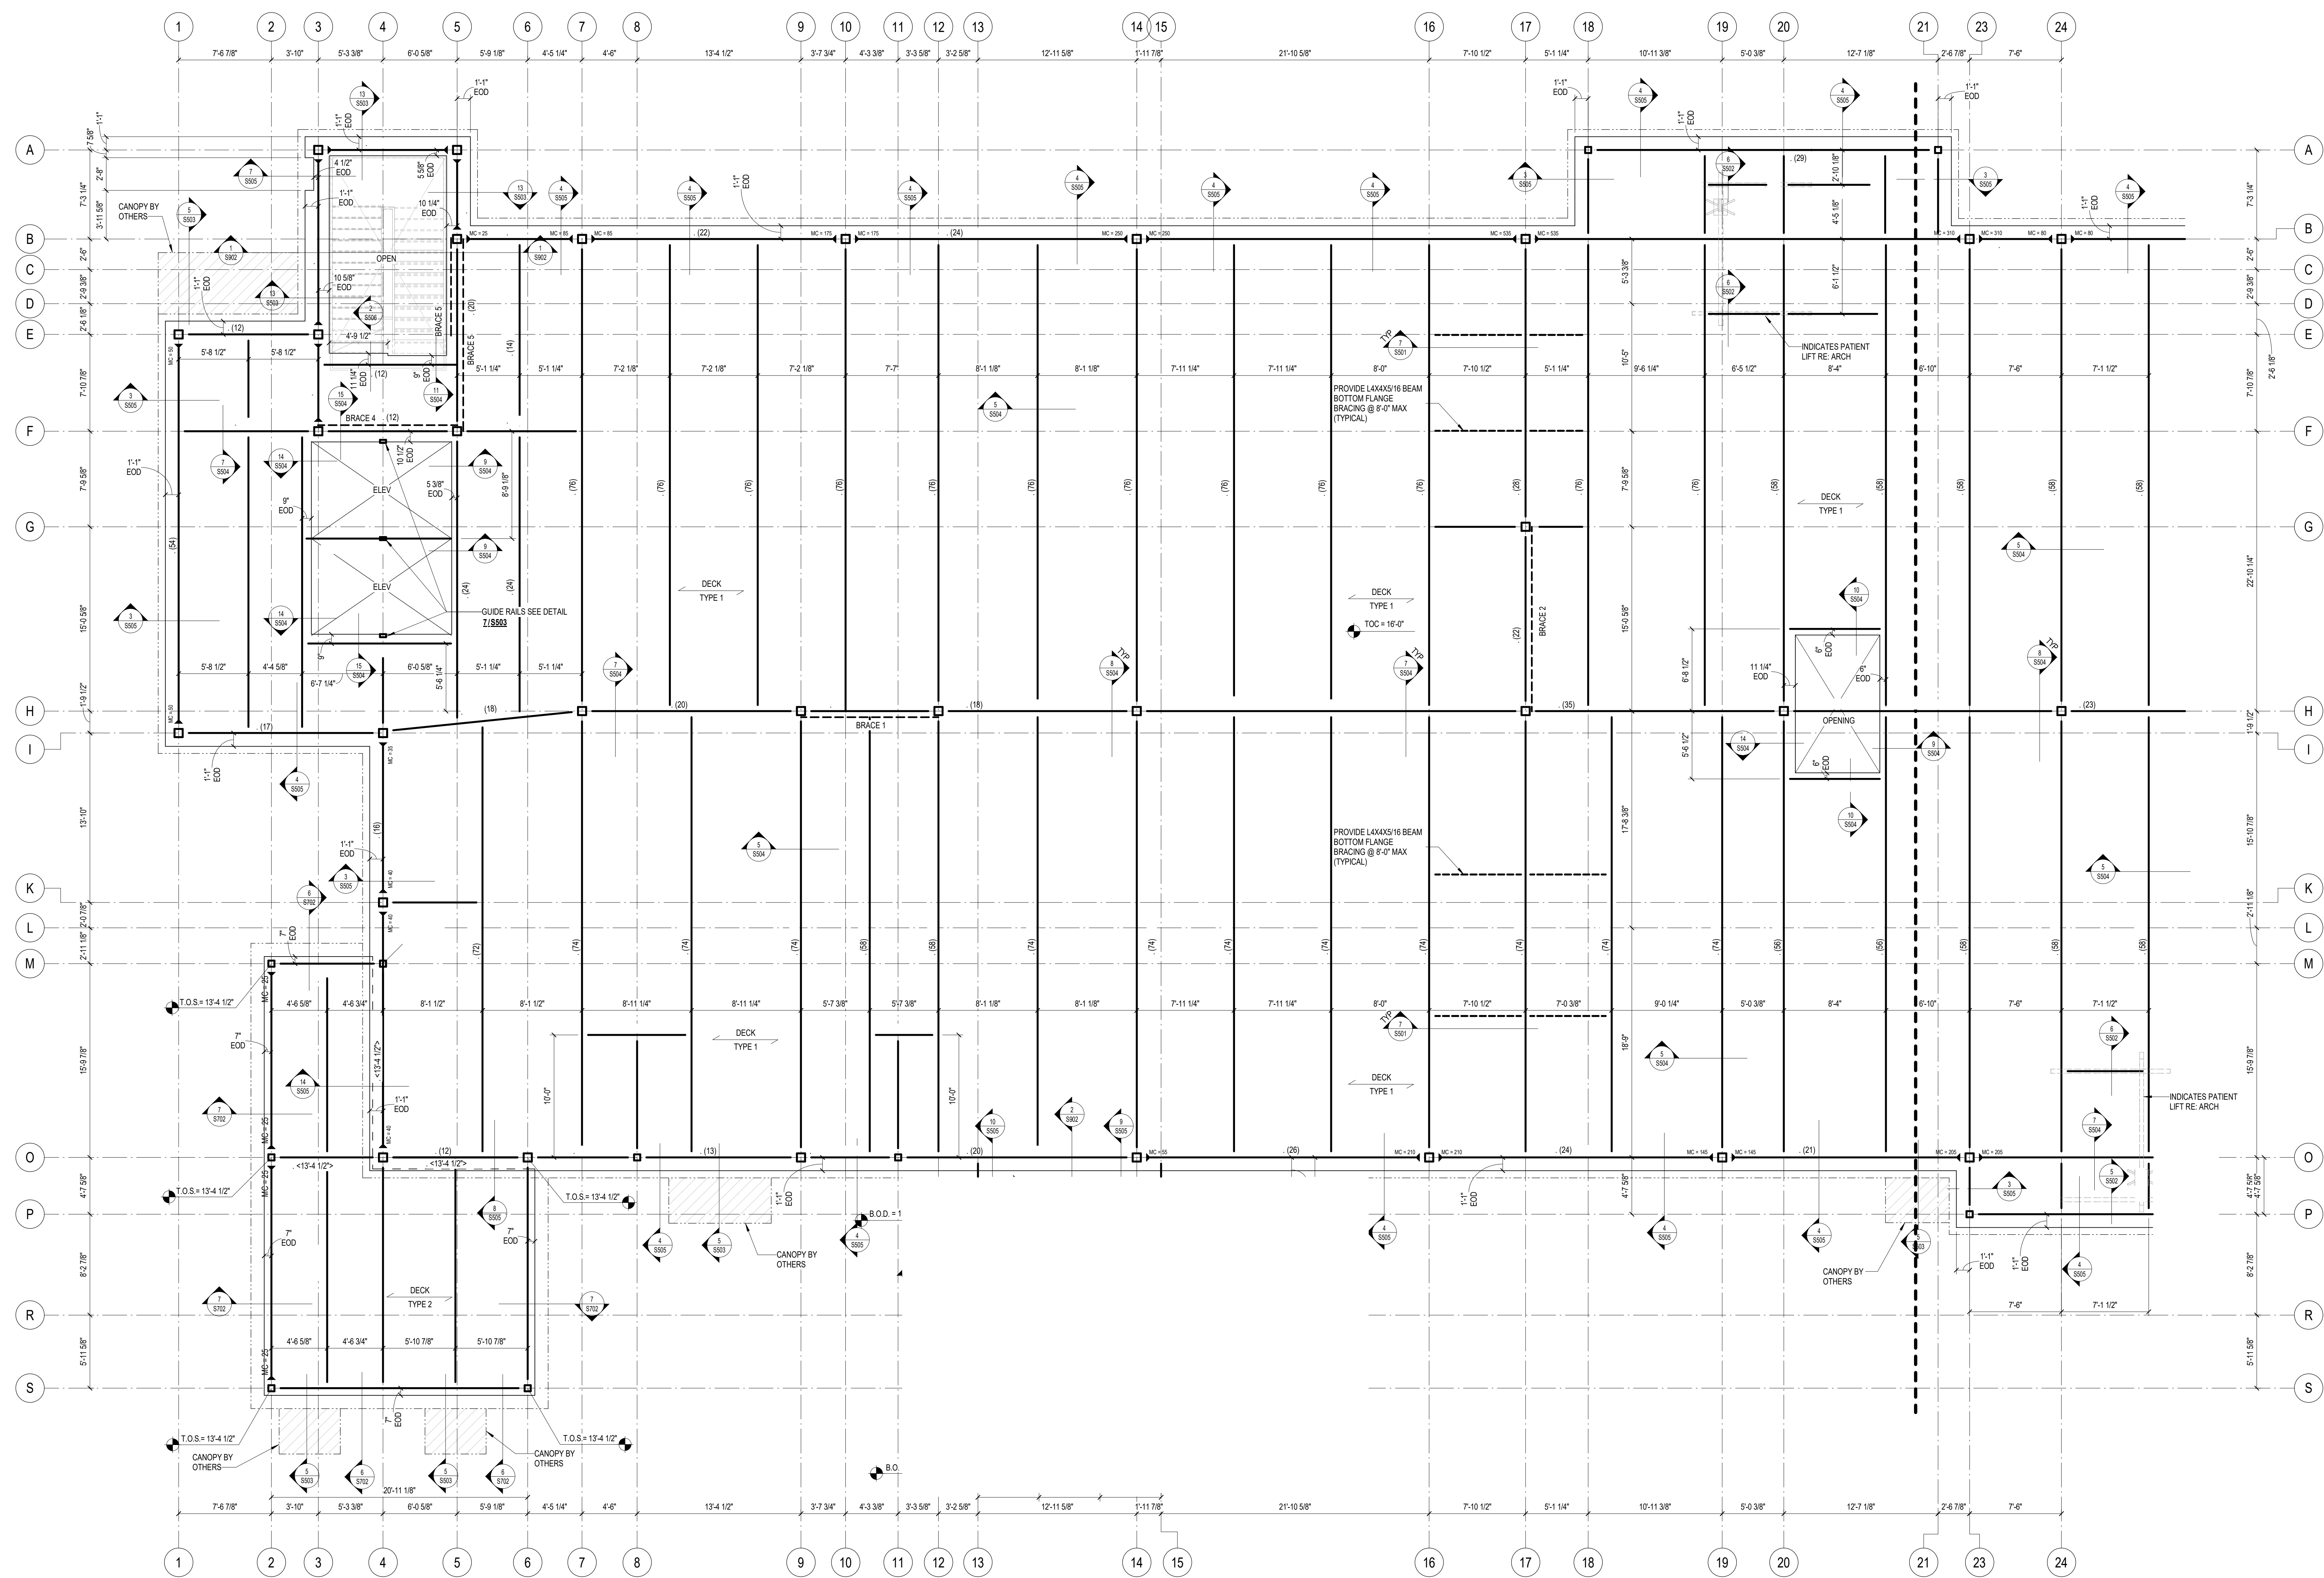

1 SECOND FLOOR FRAMING PLAN - AREA A
3/16" = 1'-0"

NOTE TO STEEL FABRICATOR:
WHERE MOMENT REACTION IS NOT SHOWN ON PLAN, CONNECTION
SHALL BE DESIGNED FOR A MINIMUM REACTION OF 25 KIP-FEET (ASD)

STEEL ROOF FRAMING NOTES:

1. ALL ELEVATIONS ARE RELATIVE TO DATUM ELEVATION.
2. * (EXAMPLE) INDICATES ROOF DECK SPAN DIRECTION AND DECK TYPE 1.
TOS ELEVATION AT ROOF DECKS ARE AT BOD, TYP. UON.
FOR DECK TYPE INFORMATION SEE: § 1501.
3. "MC = 65" INDICATES MOMENT CONNECTION REACTION IN KIP-FEET (ASD).
4. COORDINATE LOCATIONS AND SIZES OF ALL CHASES AND PENETRATIONS WITH MEP.
COORDINATE EXACT LOCATION OF ALL MEP UNITS WITH MEP.
FOR FRAMING AROUND ROOF OPENINGS SEE: § 1501.
5. FOR BRACE ELEVATIONS AND DETAILS SEE: § 801.

STEEL FRAMING NOTES

2. ALL ELEVATIONS ARE RELATIVE TO DATUM ELEVATION.
3. 1" O.C. ELEVATION AT COMPOSITE DECK IS AT 1/8" BELOW T.O. CONCRETE. TYP. UCN.
T.O. ELEVATION AT DECK TYPE IS AT 8" B.O. UCN.
FOR DECK TYPE INFORMATION RE: SD301.
3. "MC" = 65" INDICATES MOBILE CONNECTION RANGE IN KI-PEET (ASD).
4. COORDINATE LOCATIONS AND SIZES OF ALL CHASES AND PENETRATIONS WITH MEP.
COORDINATE EXACT LOCATION OF ALL MEP UNITS WITH MEP.
FOR FRAMING AROUND ROOF OPENING RE: TJS701.
5. RE: DETAILS 7 & 8 ON SHEET S303 FOR ELEVATION SUPPORT DETAILS.
6. FOR BRACE ELEVATIONS AND DETAILS RE: S801.
7. 3/4" Ø HEADED SHEAR STUDS @ 12" OC ON ALL BEAMS/GIRDERS @ COMPOSITE DECK UCN.
8. SLAB ON DECK REINFORCING 4X4 W.D.00X4.0 WELDED WIRE MESH.
9. ALL EXPOSED STEEL TO BE HOT DIP GALVANIZED.



9800 Richmond Avenue, Suite 460
Houston, Texas 77042
t 713 337 8881
Texas Registered Engineering Firm
F-003426
PROJECT #: 24-253-00

PROJECT #: 24-253-00