


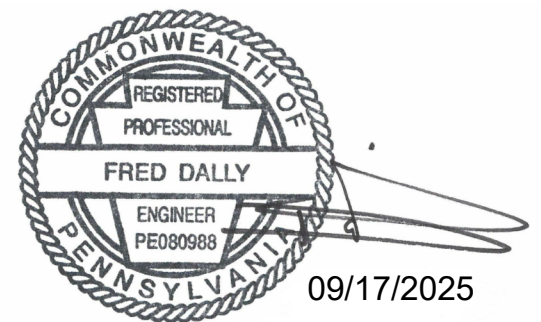

Consultants

Structural Engineer
Dally + Associates
9800 Richmond Avenue Suite 460
Houston, Texas 77042

MEP Engineer and Technology
Telios
730 Town and Country Blvd, Suite
750 Houston, TX 77042

Civil Engineers
Bohler
1515 Market Street, Suite 920
Philadelphia, PA 19102

[illegible]

Project

Emerus
Springfield
Neighborhood
Hospital

Christiana Care Community
Hospital
Springfield, PA 19064

Drawing Name:

SECOND FLOOR
FRAMING PLAN - AREA
A

Copyright (C) 2024 by PhiloWilke Partnership. All rights reserved.

This document and the information herein is the property of PhiloWike Partnership. No part hereof shall be copied, duplicated, distributed, disclosed or used to any extent whatsoever except as expressly authorized by PhiloWike Partnership. Any person, firm, or corporation receiving this document, however obtained, shall by virtue hereof, be deemed to have agreed to the foregoing restrictions and that this document will be held in trust and confidence subject only to the private use expressly authorized by PhiloWike Partnership.

Print Date / Time: 9/17/2025 12:02:13 PM


Philo/Wilke Commission Number:

S202A



9800 Richmond Avenue, Suite 460
Houston, Texas 77042
t 713 337 8881
Texas Registered Engineering Firm
F-003426
PROJECT #: 24-253-00

PROJECT #: 24-253-00

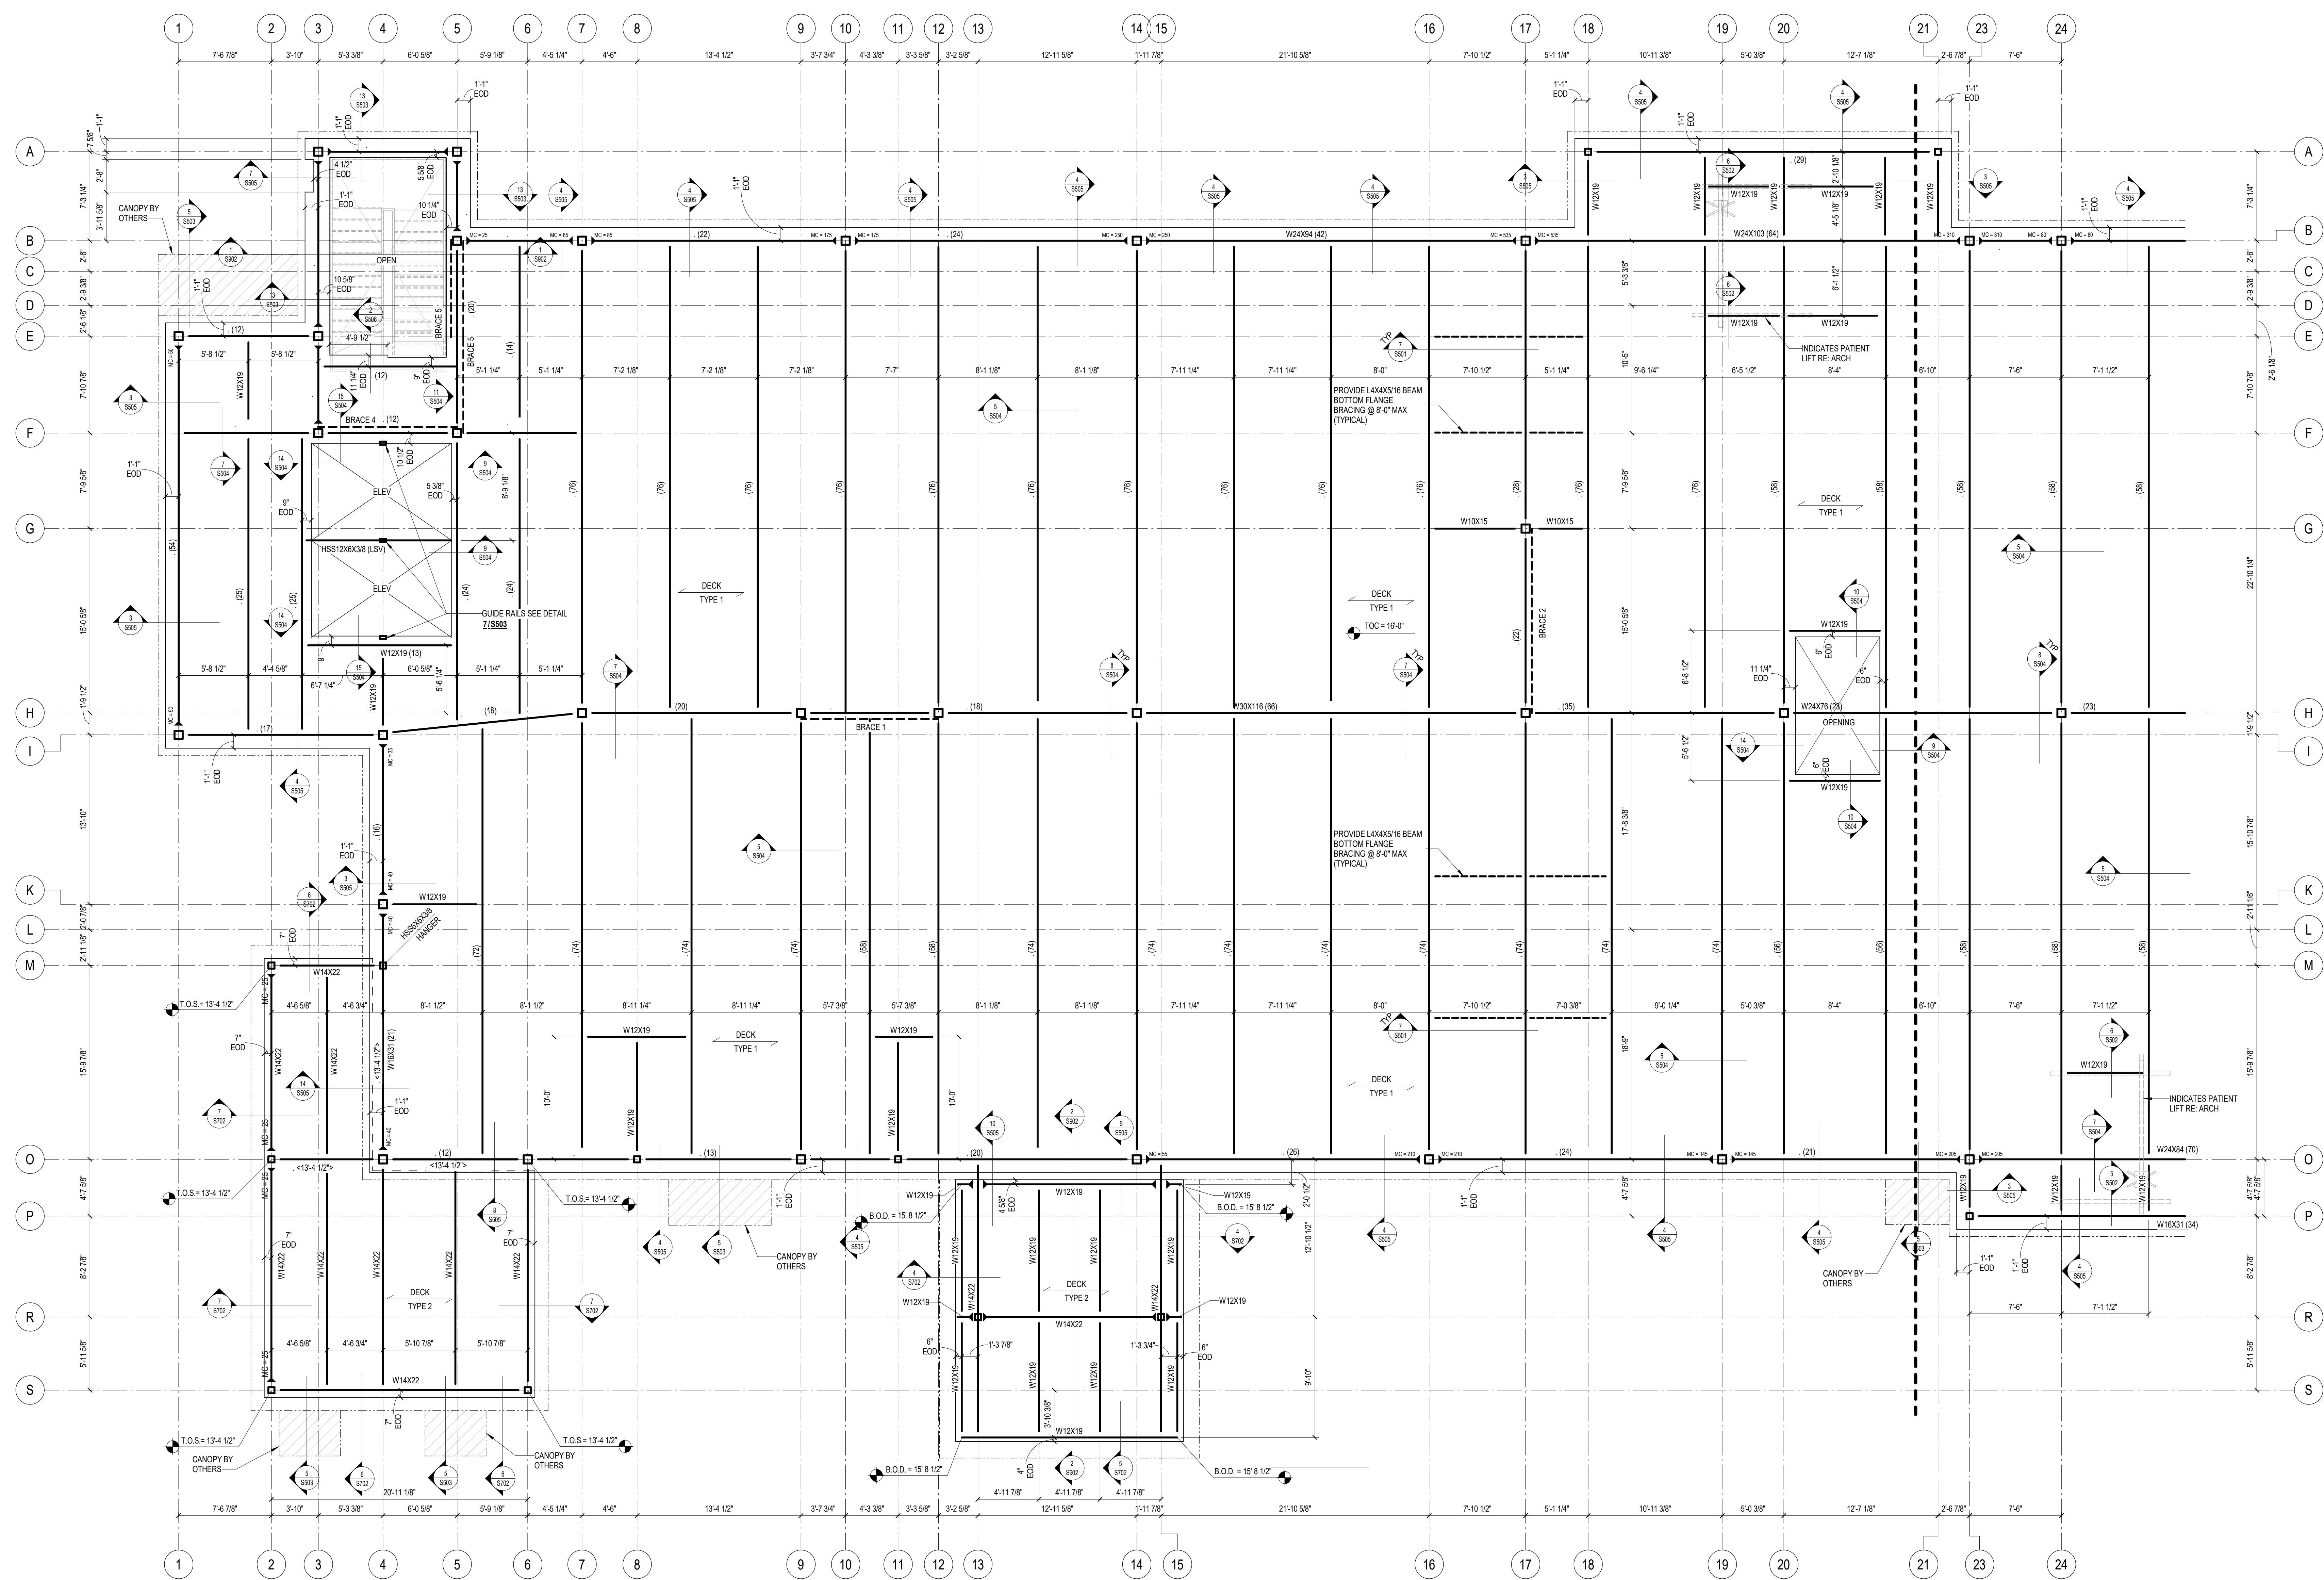

1 SECOND FLOOR FRAMING PLAN - AREA A
3/16" = 1'-0"

NOTE TO STEEL FABRICATOR:
WHERE MOMENT REACTION IS NOT SHOWN ON PLAN, CONNECTION
SHALL BE DESIGNED FOR A MINIMUM REACTION OF 25 KIP-FEET (ASD).

STEEL ROOF FRAMING NOTES:

1. ALL ELEVATIONS ARE RELATIVE TO DATUM ELEVATION.
2. *  (EXAMPLE) INDICATES ROOF DECK SPAN
TYPE 1
TOS ELEVATION AT ROOF DECKS ARE AT BOD, TYPE UON.
FOR DECK TYPE INFORMATION [RE: § 5101](#)
3. "MC = 65" INDICATES MOMENT CONNECTION REACTION IN KIP-FEET (ASD).
4. COORDINATE LOCATIONS AND SIZES OF ALL CHASES AND PENETRATIONS WITH MEP.
COORDINATE EXACT LOCATION OF ALL MEP UNITS WITH MEP.
FOR FRAMING AROUND ROOF OPENINGS [RE: § 5701](#)
5. FOR BRACE ELEVATIONS AND DETAILS [RE: § 801](#).

STEEL FRAMING NOTES

1. ALL ELEVATIONS ARE RELATIVE TO DATUM ELEVATION.
2. T.O.S. ELEVATION AT COMPOSITE DECK IS AT 12" BELOW T.O. CONCRETE. TYP UON.
3. T.O.S. ELEVATION AT DECK TYPE 2 IS AT B.O. UON.
FOR DECK TYPE INFORMATION RE: 503501.
4. "MC = 65" INDICATES MOMENT CONNECTION REACTION IN KIP-FEET (ASD).
5. COORDINATE LOCATIONS AND SIZES OF ALL CHASES AND PENETRATIONS WITH MEP.
COORDINATE EXACT LOCATION OF ALL MEP UNITS WITH MEP.
FOR FRAMING AROUND ROOF OPENING RE: 575071.
6. RE- DETAILS 7 & 8 ON SHEET \$5033 FOR ELEVATOR SUPPORT DETAILS.
7. FOR BRACE ELEVATIONS AND DETAILS RE: \$501.
8. 7/34" Ø HEADED SHEAR STUDS @ 12" OC ON ALL BEAMS/ORDERS @ COMPOSITE DECK UON.
9. SLAB ON DECK REINFORCING 4X4 W40X44.0 WELDED WIRE MESH
10. ALL EXPOSED STEEL TO BE HOT DP GALVANIZED.